


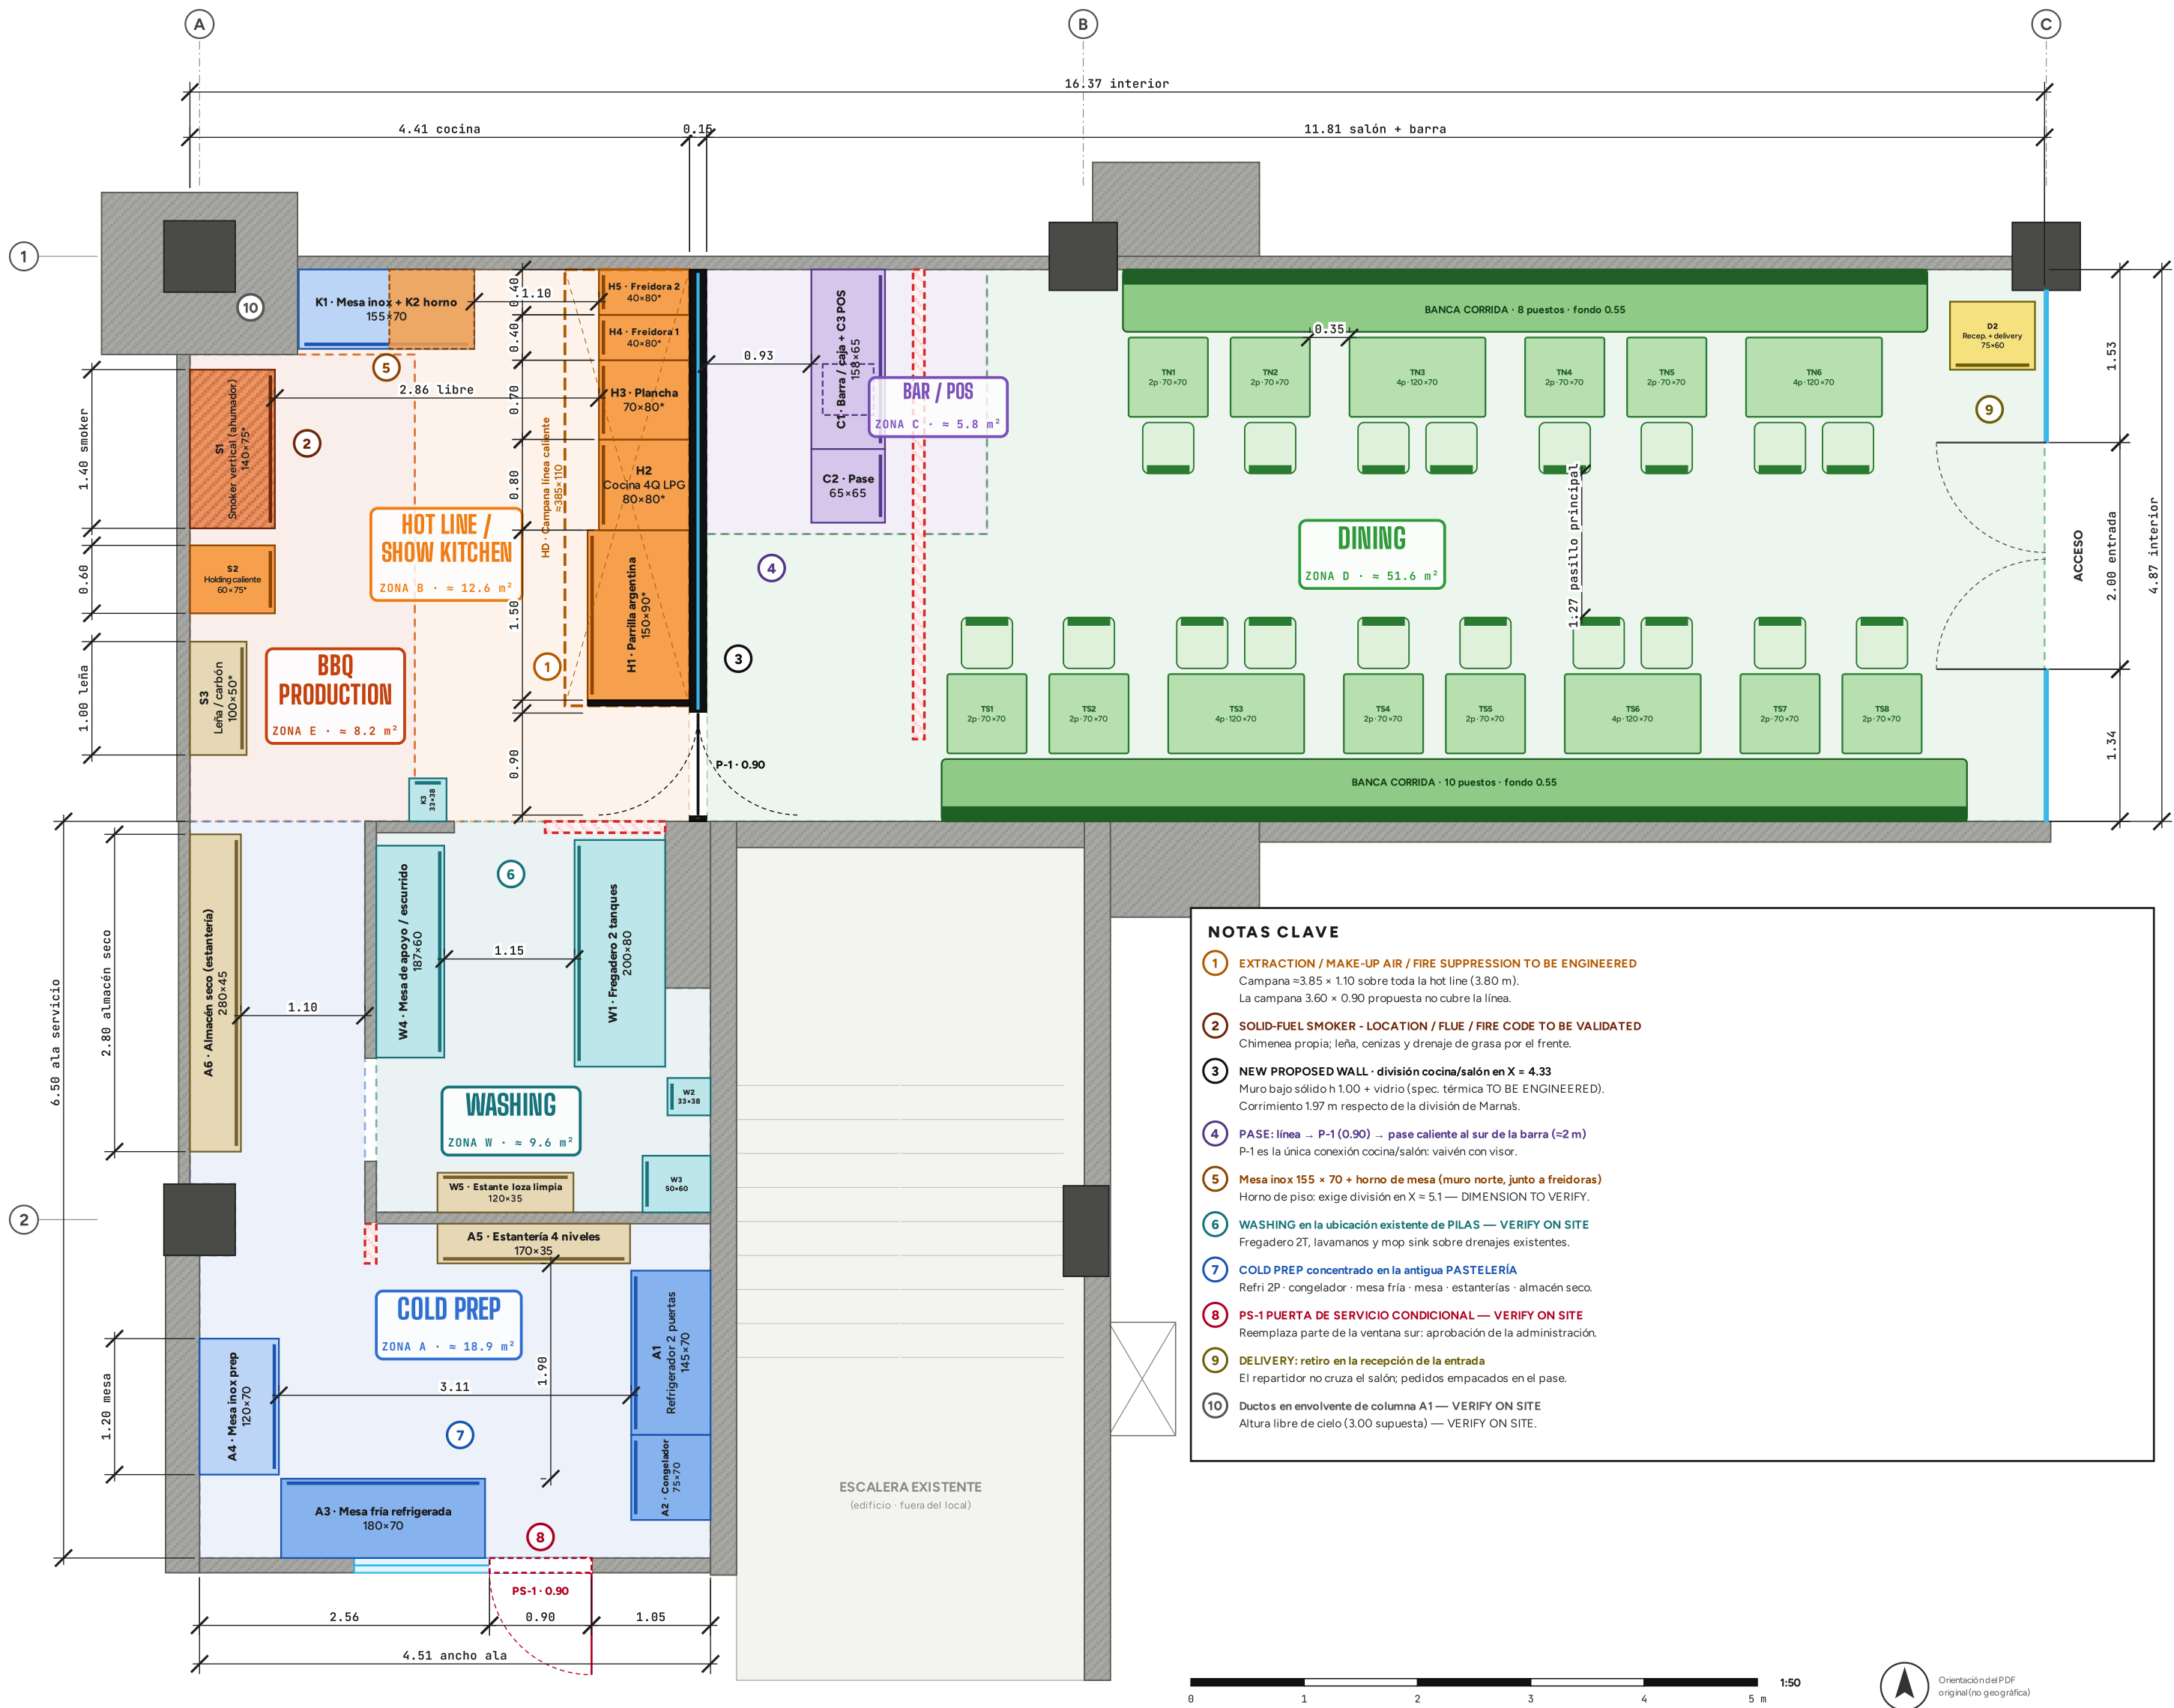

CUADRO DE EQUIPOS

- H1 Parrilla argentina
- H2 Cocina LPG 4 quemadores
- H3 Plancha
- H4 Freidora 1
- H5 Freidora 2
- K2 Horno (sobre mesa)
- S2 Holding caliente
- HD Campana línea caliente
- S1 Smoker vertical (ahumador)

frente x fondo x alto (m) - * = DIMENSION TO VERIFY

- A4 Mesa de trabajo inox (prep fría)
- K1 Mesa de trabajo inox
- A1 Refrigerador 2 puertas
- A2 Congelador vertical
- A3 Mesa fría refrigerada
- K3 Lavamanos cocina (recomendado)
- W1 Fregadero 2 tanques
- W2 Lavamanos
- W3 Pileta / mop sink

- W4 Mesa de apoyo / escumido
- A5 Estantería 4 niveles
- A6 Almacén seco (estantería)
- S3 Leña / carbón (rack metálico)
- W5 Estante loza limpia
- C1 Barra / caja + bebidas
- C2 Pase / pickup caliente
- C3 POS
- D2 Recepción + staging / retiro delivery

- 1.87x0.60x0.90
- 1.70x0.35x1.80
- 2.80x0.45x2.00
- 1.00x0.50x1.20*
- 1.20x0.35x1.80
- 1.50x0.65x1.05
- 0.65x0.65x1.05
- 0.45x0.45x1.10
- 0.75x0.60x1.05

LEYENDA

- EXISTING WALL (gris - se mantiene)
- WALL TO DEMOLISH (rojo punteado)
- NEW PROPOSED WALL (negro)
- Nueva división: base sólida + vidrio
- Fuego / hot line (naranja)
- Campana (proyección en altura)
- Smoker combustible sólido
- Refrigeración / prep fría (azul)
- Mesas de trabajo inox
- Lavado
- Almacén / leña
- Barra / POS / pase
- Delivery / recepción
- Dining: mesas, sillas, bancas (verde)

CIFRAS CLAVE (MEDIDAS SOBRE LA PLANTA)

Asientos en salón	36
Corrimiento división cocina/salón	1.97 m
B - HOT LINE / SHOW KITCHEN	12.6 m²
E - BBQ PRODUCTION	8.2 m²
W - WASHING	9.6 m²
A - COLD PREP	18.9 m²
C - BAR / POS	5.8 m²
D - DINING	51.6 m²
Ancho mín. Pase → mesas (pasillo central)	1.28 m
Ancho mín. Línea → puerta P-1 → pase	0.90 m
Ancho mín. Salón → puerta P-1 → lavado	0.92 m
Ancho mín. Frio → prep → pasillo limpio	1.00 m
Línea caliente / campana dibujada	3.80 / 3.85 m
Asientos con vista a la parrilla	100 %

NOTAS

Test-fit conceptual: validar con arquitecto e ingenierías.
Geometría base: vectores del PDF Mama's (1:50). Cotas ±2 cm.
Hot line fija sobre la división con el salón (cliente).
BBQ production (smoker + holding) en el muro del fondo.
Lavado en PILAS existentes: cold prep en ex-PASTELERÍA.
*/ punto rojo = DIMENSION TO VERIFY (equipo sin ficha).
Altura libre de cielo y ductos existentes: VERIFY ON SITE.
Campana, aire de reposición, supresión y gas: TO BE ENGINEERED.
Egreso, sentido de puertas y ocupación: validar Bomberos/NFPA 101.

NOTAS CLAVE

- EXTRACTION / MAKE-UP AIR / FIRE SUPPRESSION TO BE ENGINEERED**
Campana ≈3.85 x 1.10 sobre toda la hot line (3.80 m).
La campana 3.60 x 0.90 propuesta no cubre la línea.
- SOLID-FUEL SMOKER - LOCATION / FLUE / FIRE CODE TO BE VALIDATED**
Chimenea propia; leña, cenizas y drenaje de grasa por el frente.
- NEW PROPOSED WALL - división cocina/salón en X = 4.33**
Muro bajo sólido h 1.00 + vidrio (spec. térmica TO BE ENGINEERED).
Corrimiento 1.97 m respecto de la división de Mama's.
- PASE: línea → P-1 (0.90) → pase caliente al sur de la barra (≈2 m)**
P-1 es la única conexión cocina/salón: vaivén con visor.
- Mesa inox 155 x 70 + horno de mesa (muro norte, junto a freidoras)**
Horno de piso: exige división en X = 5.1 — DIMENSION TO VERIFY.
- WASHING en la ubicación existente de PILAS — VERIFY ON SITE**
Fregadero 2T, lavamanos y mop sink sobre drenajes existentes.
- COLD PREP concentrado en la antigua PASTELERÍA**
Refri 2P - congelador - mesa fría - mesa - estanterías - almacén seco.
- PS-1 PUERTA DE SERVICIO CONDICIONAL — VERIFY ON SITE**
Reemplaza parte de la ventana sur: aprobación de la administración.
- DELIVERY: retiro en la recepción de la entrada**
El repartidor no cruza el salón; pedidos empacados en el pase.
- Ductos en envoltorio de columna A1 — VERIFY ON SITE**
Altura libre de cielo (3.00 supuesta) — VERIFY ON SITE.

LAVA

CONTEMPORARY FIRE & BBQ

Local ex-Manna's - Terrazas Lindora, Santa Ana

A-101 · Planta propuesta (test-fit)

Zonificación operativa, equipos con nombre y medida, mobiliario y cotas


TEST-FIT CONCEPTUAL · NO ES PLANO CONSTRUCTIVO

Base: vectores del PDF Mama's RevB Opcción (1:50) Validar con arquitecto e ingenierías.

Escala 1:50 en A2 · cotas en metros · v2.0 · 2026-09-25

LÁMINA

A-101

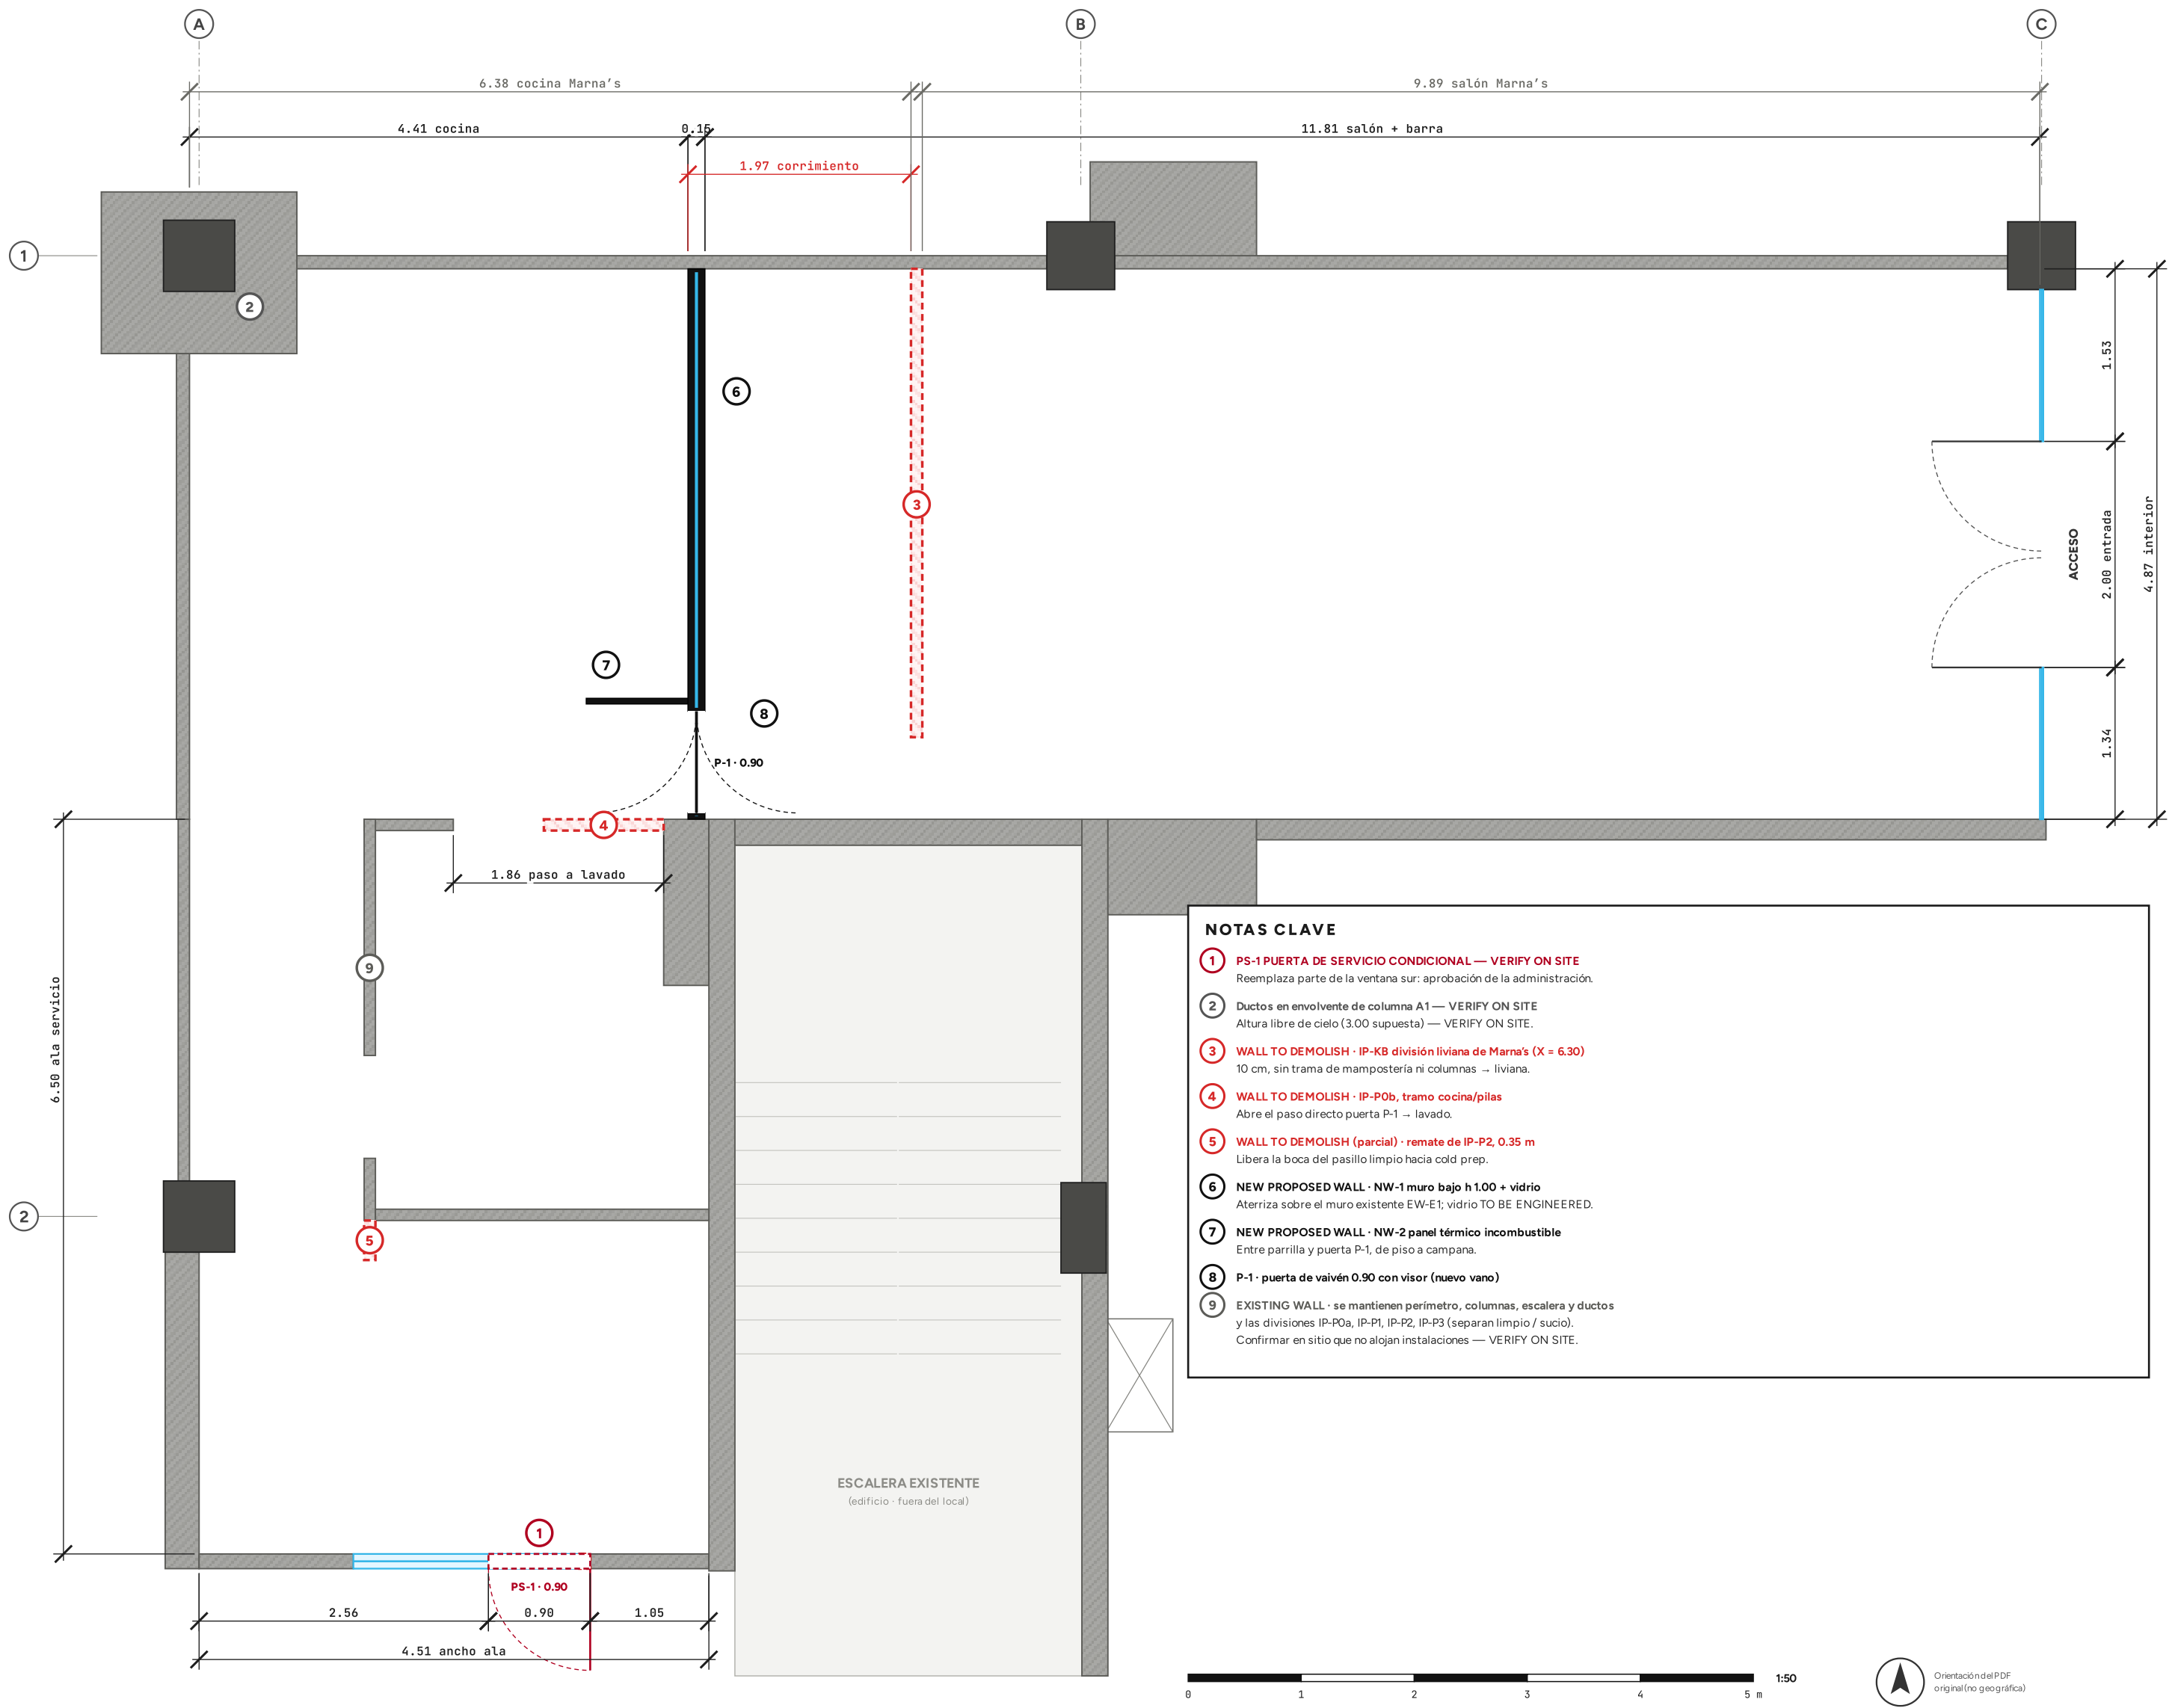

EVALUACIÓN DE MUROS EXISTENTES (lectura del PDF + criterio · VERIFY ON SITE)

ID	Descripción
EW-N1	Muro norte (11.6 cm) cocina/barra
EW-N2	Muro norte salón
EW-PIL	Envolvente de columna A1 con 4-5 celdas de ducto (X). Uso de ductos: VERIFY
EW-W1	Muro oeste cocina
EW-W2	Muro oeste ala (tramo norte)
EW-W3	Muro oeste ala (tramo sur). Hoja de puerta dibujada por el exterior (Y 10).
EW-S1	Muro sur ala
EW-S2	Muro sur ala
EW-E1	Muro este ala tramo norte (40 cm, incluye ducto S3)
EW-E2	Muro oeste de la escalera = muro este del ala
EW-STN	Muro norte de escalera (colinda con barra/salón)
EW-SD	Muro sur salón (18 cm)
IP-KB	División actual cocina / barra-postres (verde en PDF). Paso libre al sur Y
IP-P0a	División cocina/pilas (oeste de ventana platos sudos)
IP-P0b	División cocina/pilas (este de ventana platos sudos)
IP-P1	División pasillo/pilas tramo norte
IP-P2	División pasillo/pilas tramo sur
IP-P3	División pilas / pastelería

Esp.	Trama	Lectura estructural
12 cm	si	perimetral - mantener
12 cm	si	perimetral - mantener
143 cm	si	estructural + ductos - mantener
12 cm	si	perimetral - mantener
10 cm	si	perimetral - mantener
30 cm	si	perimetral - mantener
13 cm	si	perimetral - mantener
13 cm	si	perimetral - mantener
40 cm	si	perimetral grueso con ducto S3 - mantener
23 cm	si	muro de escalera - mantener
23 cm	si	muro de escalera - mantener
18 cm	si	perimetral - mantener
10 cm	no	LIVIANA (10 cm, sin trama de mampostería, sin columnas) - demo
10 cm	si	liviana 10 cm
10 cm	si	liviana 10 cm
10 cm	si	liviana 10 cm
10 cm	si	liviana 10 cm
10 cm	si	liviana 10 cm

Acción
EXISTING WALL · MANTENER
EXISTING WALL · MANTENER
EXISTING WALL · MANTENER
EXISTING WALL · MANTENER
EXISTING WALL · MANTENER
EXISTING WALL · MANTENER
EXISTING WALL · MANTENER
RECORTE CONDICIONAL (PS-1)
EXISTING WALL · MANTENER
EXISTING WALL · MANTENER
EXISTING WALL · MANTENER
EXISTING WALL · MANTENER
EXISTING WALL · MANTENER
WALL TO DEMOLISH
EXISTING WALL · MANTENER
WALL TO DEMOLISH
EXISTING WALL · MANTENER
RECORTE PARCIAL
EXISTING WALL · MANTENER

LEYENDA

	EXISTING WALL (gris - se mantiene)
	WALL TO DEMOLISH (rojo punteado)
	NEW PROPOSED WALL (negro)
	Nueva división: base sólida + vidrio

WALL TO DEMOLISH (LIVIANAS)

IP-KB	4.14 m
IP-P0b	1.06 m
IP-P2 (parcial)	0.35 m
EW-S2 (condicional)	0.13 m

NEW PROPOSED WALL / VANOS

NW-1 · Muro bajo h 1.00 + vidrio	4.87 m
NW-2 · Panel térmico	0.90 m
P-1 · double acting door	0.90 m
PS-1 · service door (condicional)	0.90 m

CRITERIO ESTRUCTURAL

Se mantienen columnas A1, B1, C1, A2, escalera, ductos y perímetro. Solo se demuelen divisiones livianas de 10 cm (IP-KB, IP-P0b). IP-KB no tiene trama de mampostería ni columnas: liviana. IP-P0a, IP-P1, IP-P2 e IP-P3 se conservan (separan limpio/sucio). La nueva división ateniza sobre el muro existente EW-E1. Confirmar en sitio que ninguna división aloja instalaciones. PS-1 solo con aprobación: abrir vano en ventana sur.

LAVA

CONTEMPORARY FIRE & BBQ

Local ex-Marna's · Terrazas Lindora, Santa Ana

A-102 · Existente / demolición / nuevo

EXISTING WALL · WALL TO DEMOLISH · NEW PROPOSED WALL · corrimiento de la división


TEST-FIT CONCEPTUAL · NO ES PLANO CONSTRUCTIVO

Base: vectores del PDF Marna's RevB Opodón I (1:50) Validar con arquitecto e ingenieros.

Escala 1:50 en A2 · cotas en metros · v2.0 · 2026-09-25

LÁMINA

A-102

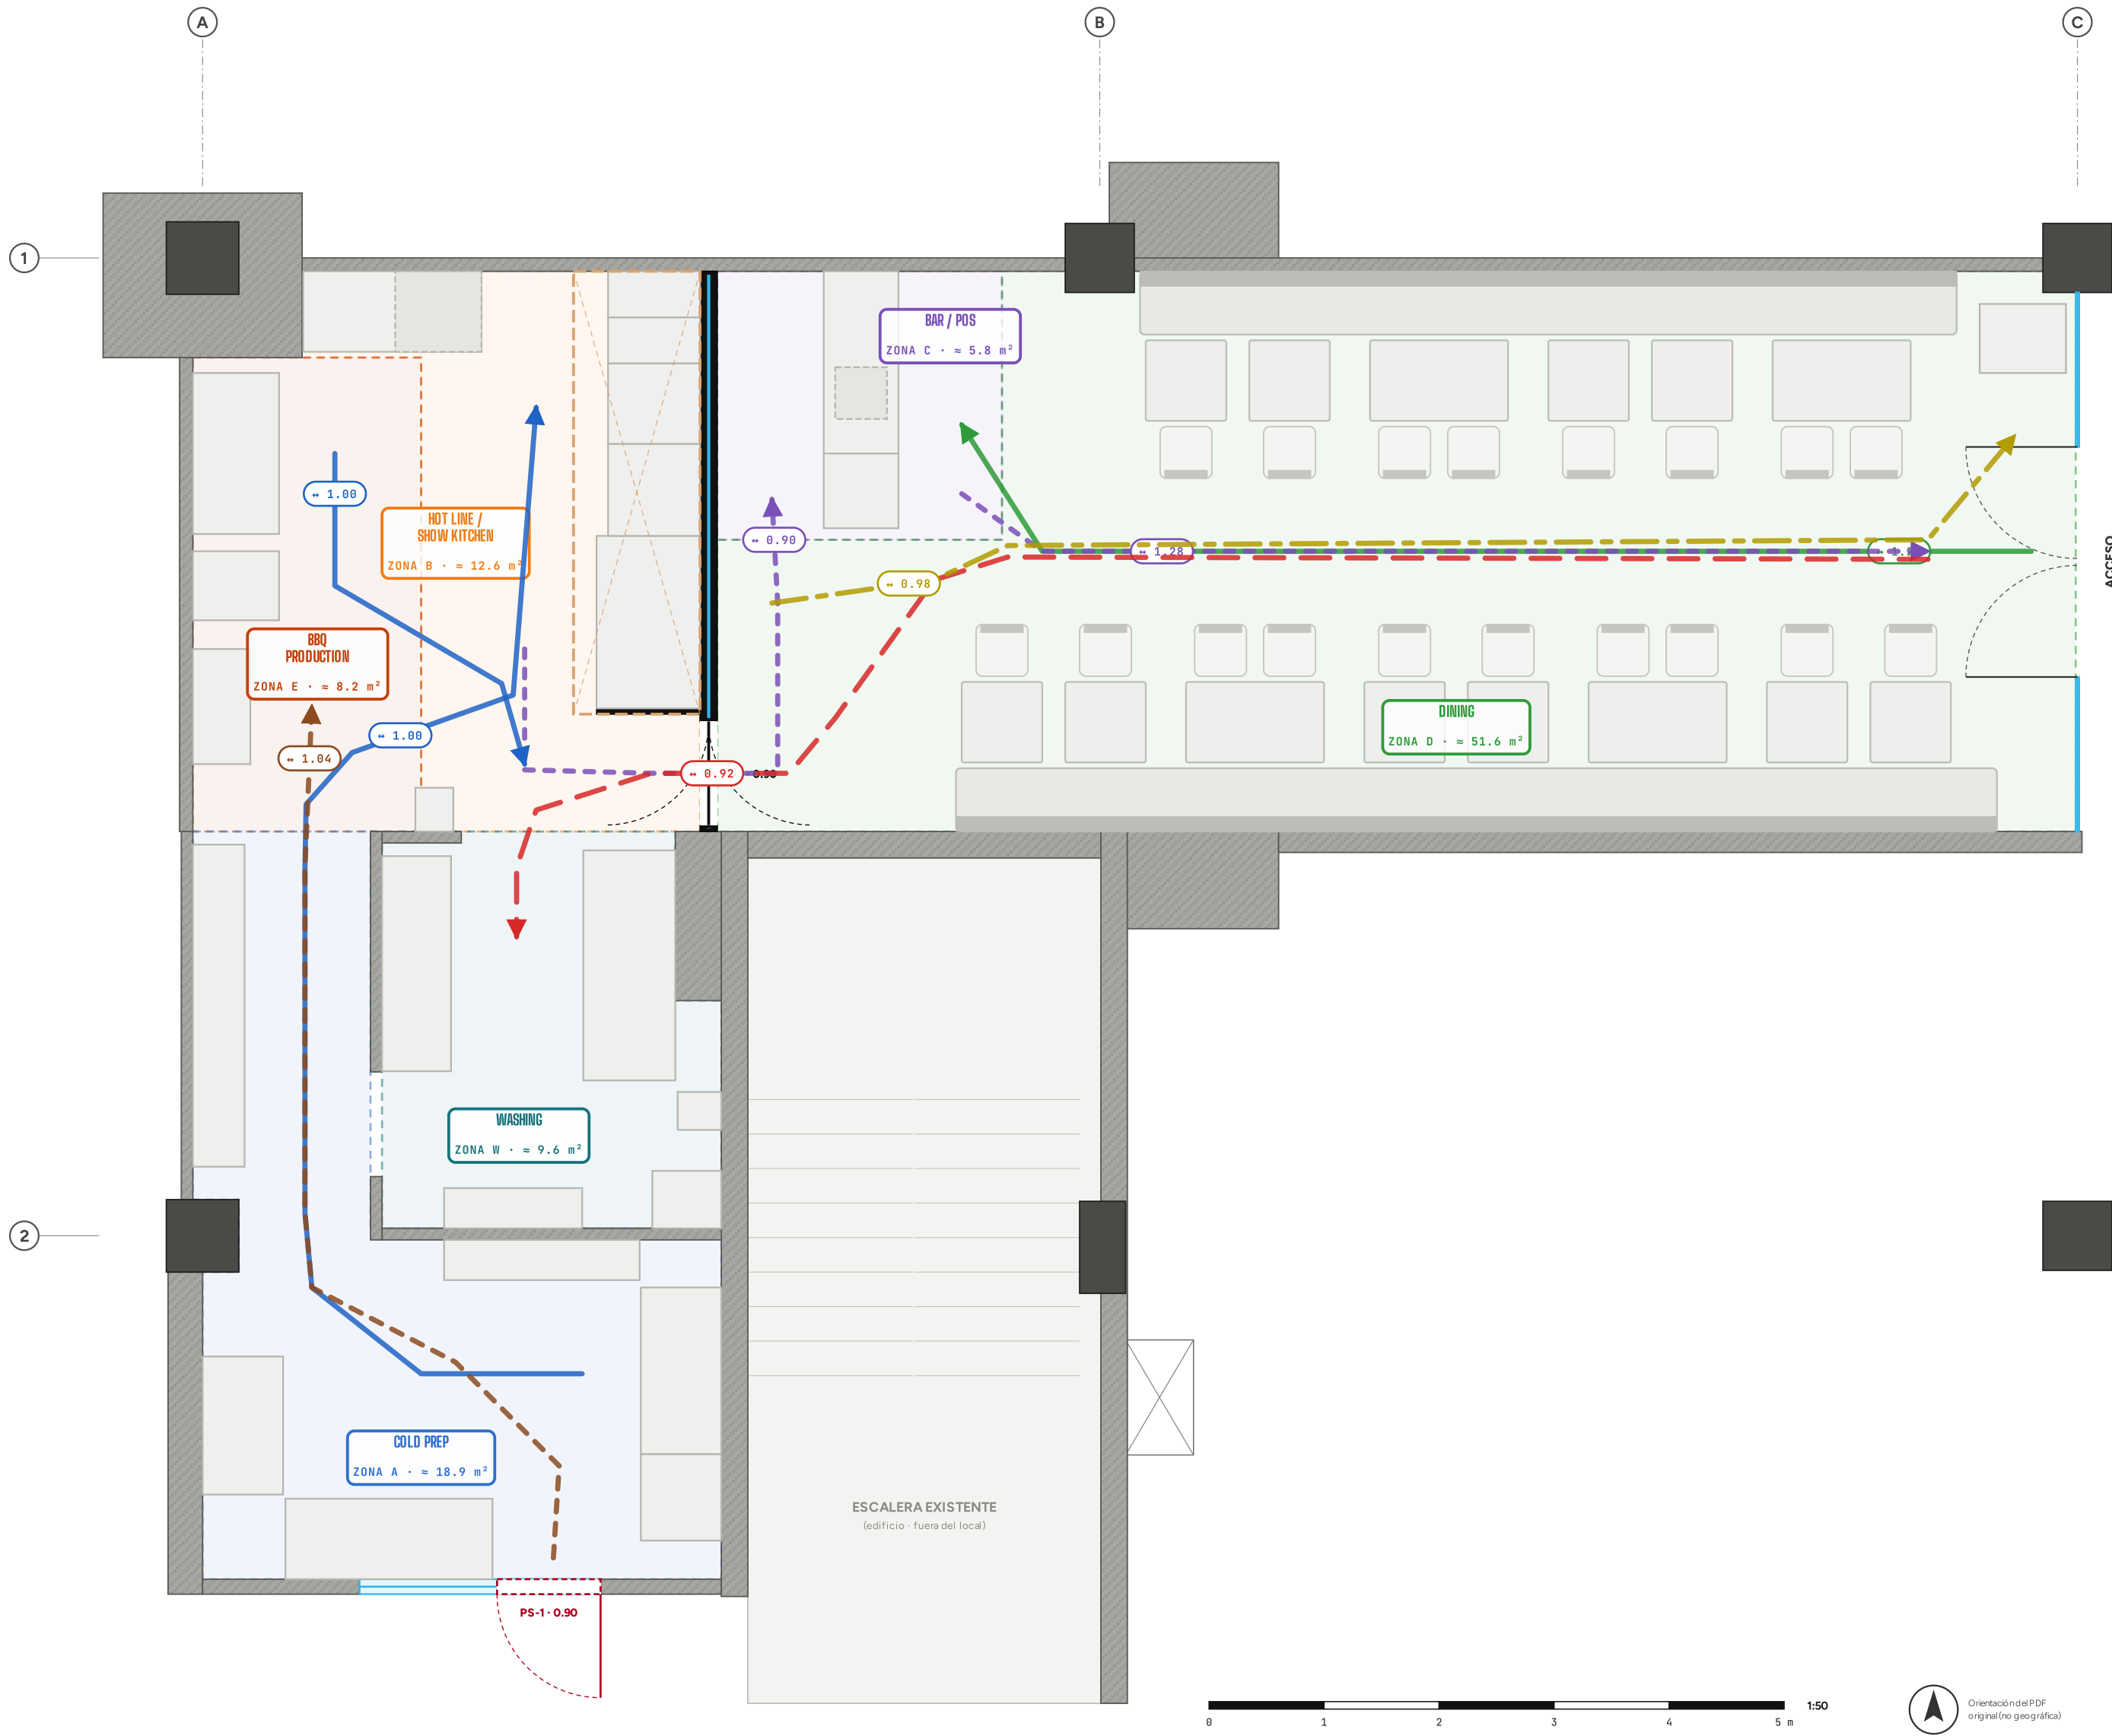

LÓGICA OPERATIVA (fijada por el cliente)



La loza sucia entra por P-1 y baja directo al lavado (antiguas PILAS); no pasa por COLD PREP ni por el pasillo limpio del muro oeste.

FLUJOS

- Cientes
- Platos: línea → P-1 → pase → mesas
- Flujo sucio (salón → lavado)
- Flujo limpio (frío → prep → línea / BBQ)
- Delivery (pedido → recepción)
- Leña / cenizas (PS-1 condicional)

ANCHO LIBRE MÍNIMO MEDIDO (M)

Entrada → barra / caja	1.28 (≥1.10)
Pase → mesas (pasillo central)	1.28 (≥1.10)
Línea → puerta P-1 → pase	0.90 (≥0.90)
Salón → puerta P-1 → lavado	0.92 (≥0.90)
Frio → prep → pasillo limpio → línea	1.00 (≥1.00)
Smoker → holding → línea / pase	1.00 (≥1.00)
Pase → staging en recepción (retiro sin cruz	0.98 (≥0.90)
Leña / cenizas → PS-1 (condicional, fuera de	1.04 (≥0.90)

Medido sobre la planta entre equipos, sillas ocupadas y muros a lo largo de cada recorrido.

Principal objetivo 1.10-1.20 m - secundaria ≥ 0.90 m.

SEPARACIÓN LIMPIO / SUCIO

Limpio: cold prep → pasillo oeste → línea → P-1 → pase.
Sucio: salón → P-1 → gira al sur → fregadero (≈15 m).
La ruta sucia no pasa por el pasillo limpio ni por cold prep.
Smoker → holding → línea / pase por el frente del muro oeste.
P-1 es la única conexión cocina/salón: platos y loza comparten puerta.

LAVA

CONTEMPORARY FIRE & BBQ

Local ex-Marna's - Terrazas Lindora, Santa Ana

A-103 · Flujos y circulaciones

Limpio / sucio / platos / clientes / delivery / combustible - anchos mínimos medidos

TEST-FIT CONCEPTUAL · NO ES PLANO CONSTRUCTIVO

Base: vectores del PDF Marna's RevB Opción 1 (1:50) Validar con arquitecto e ingenieros.

Escala 1:50 en A2 · cotas en metros · v2.0 · 2026-09-25

LÁMINA

A-103